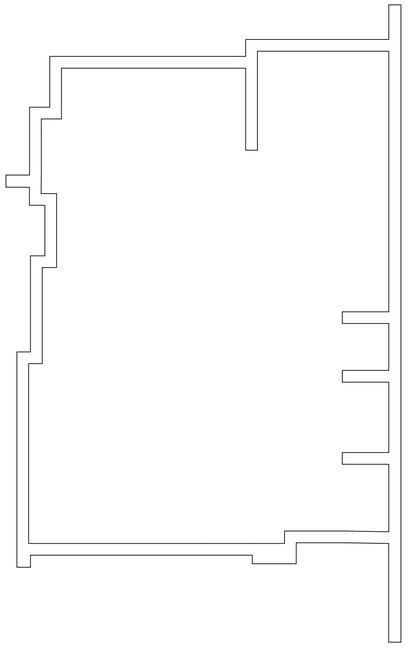

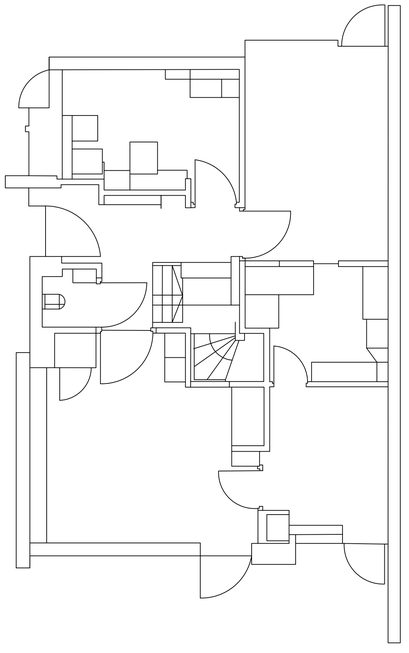

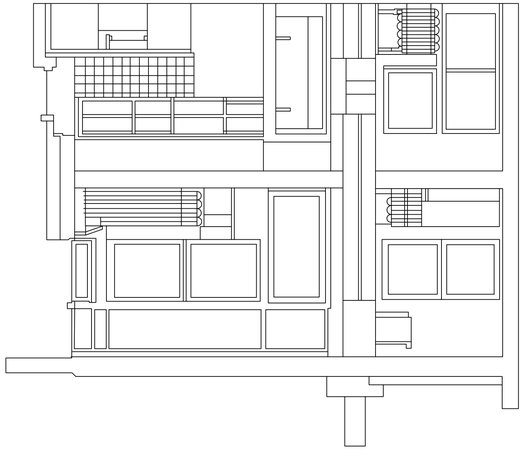

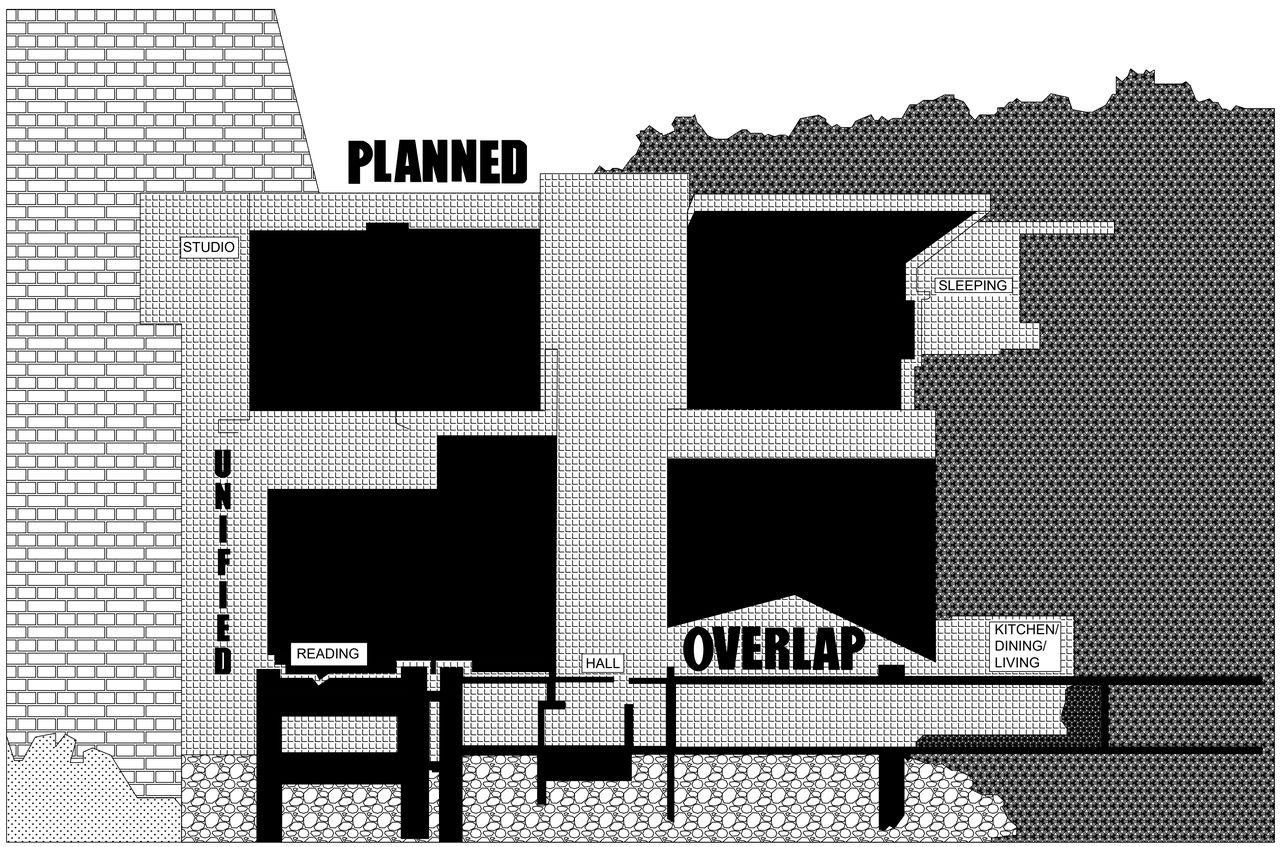
PLANNED
STUDIO
SLEEPING
UNIFIED
READING
HALL
OVERLAP
KITCHEN/
DINING/
LIVING

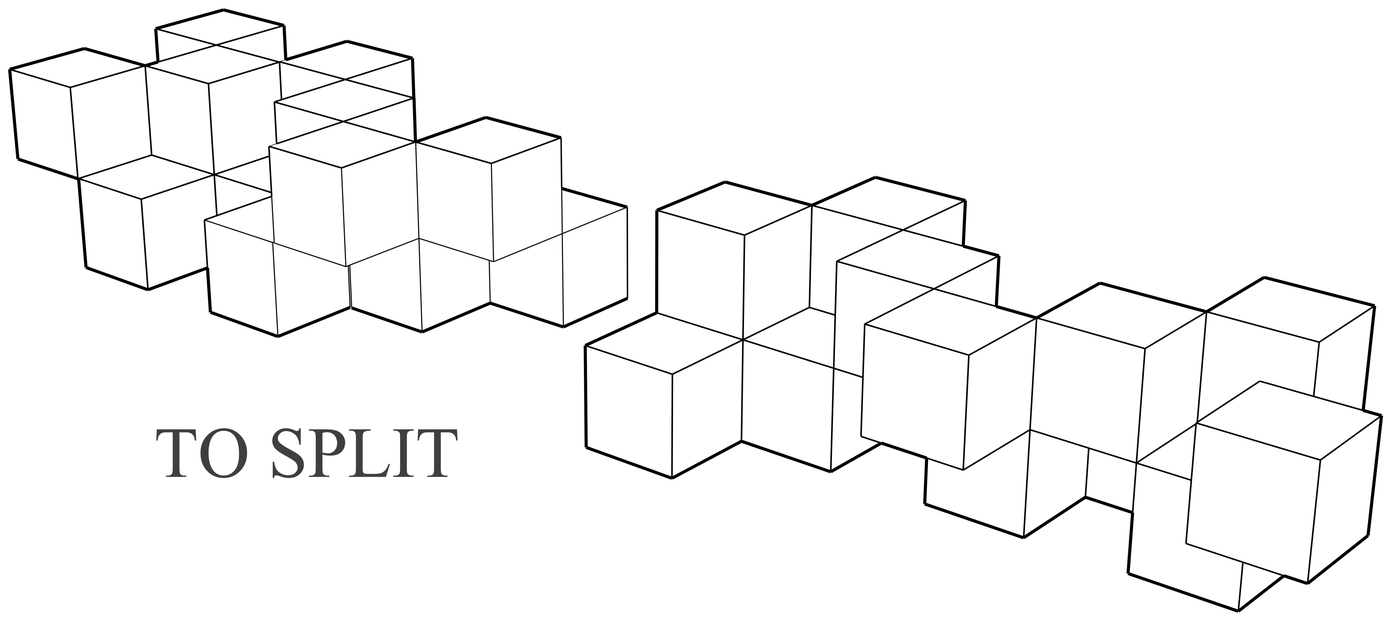

TO SPLIT

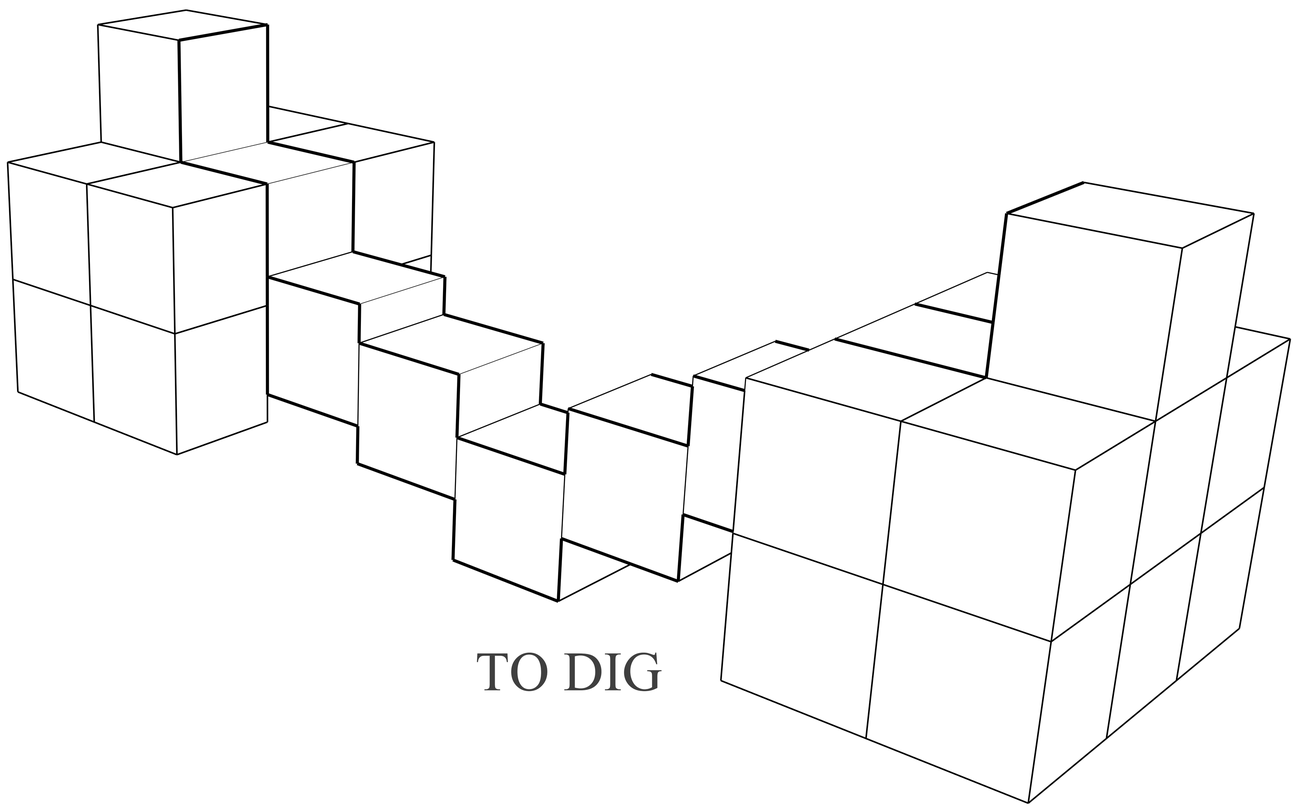

TO DIG

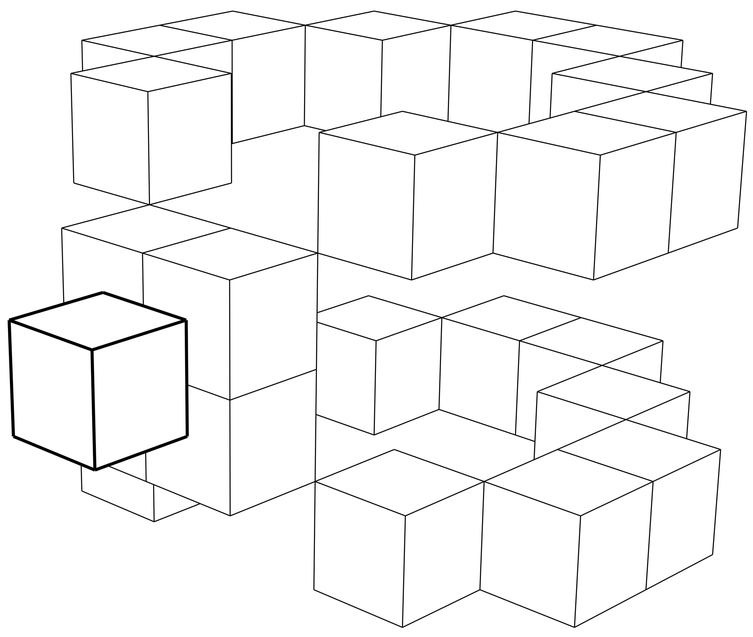
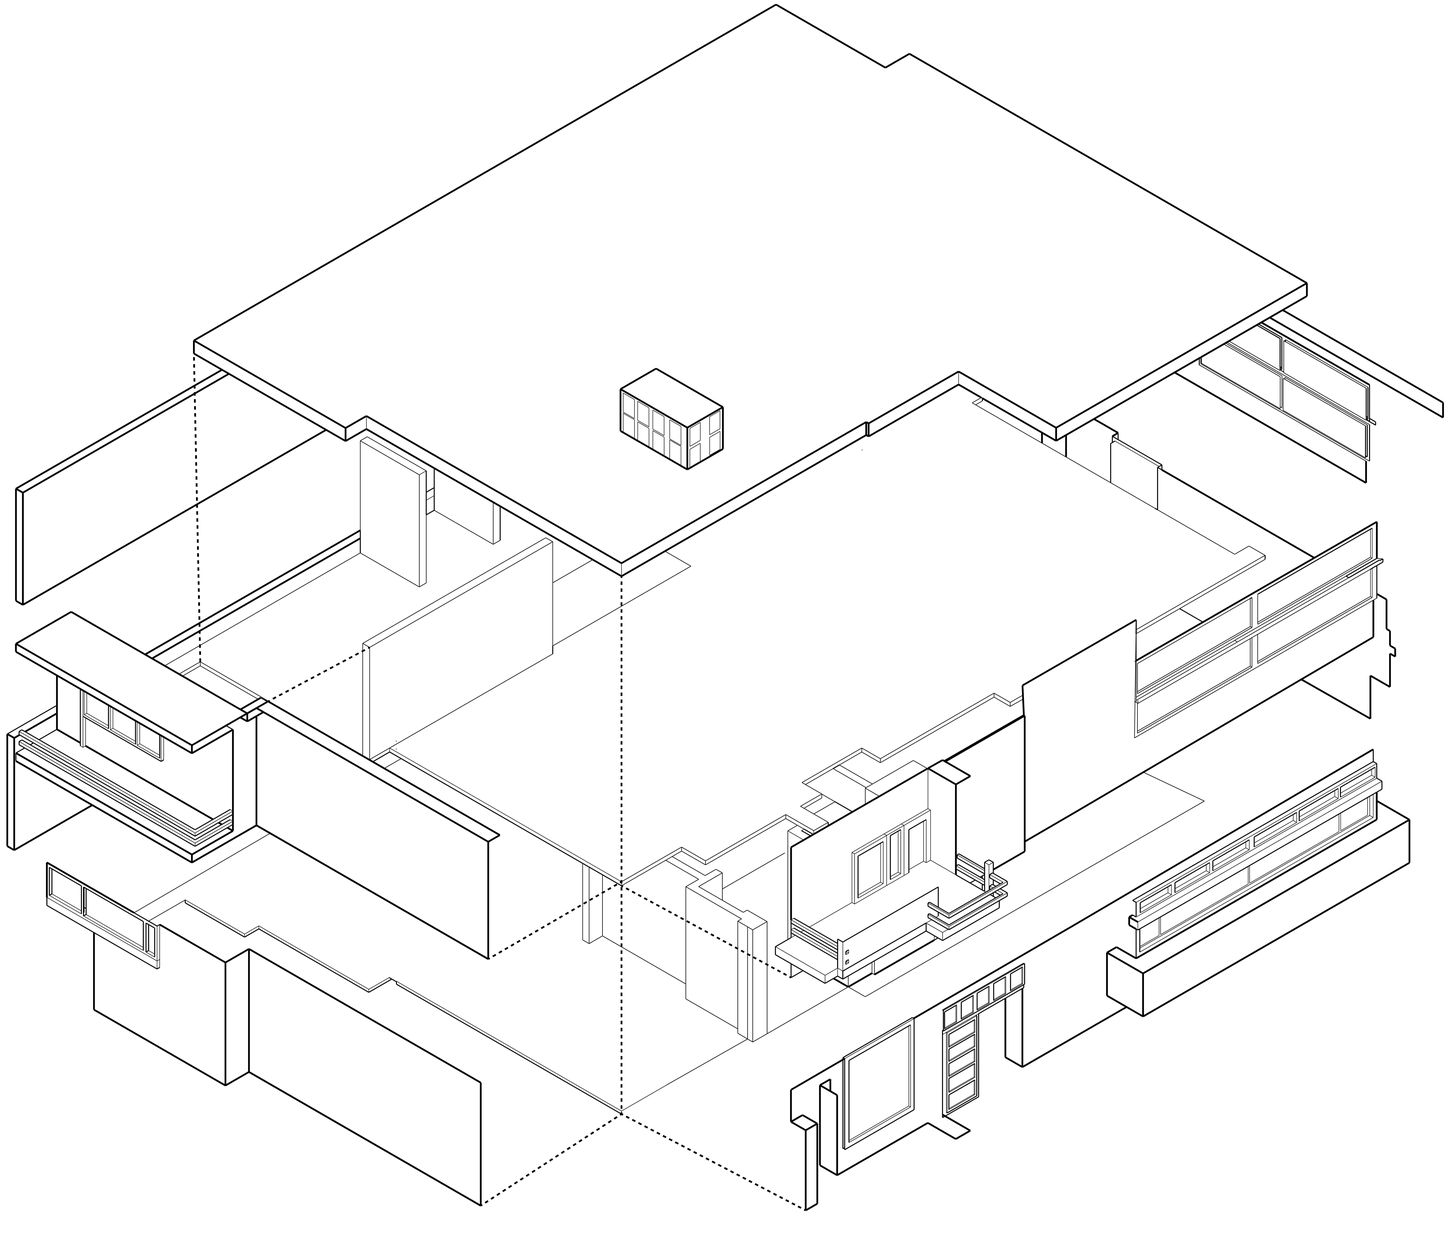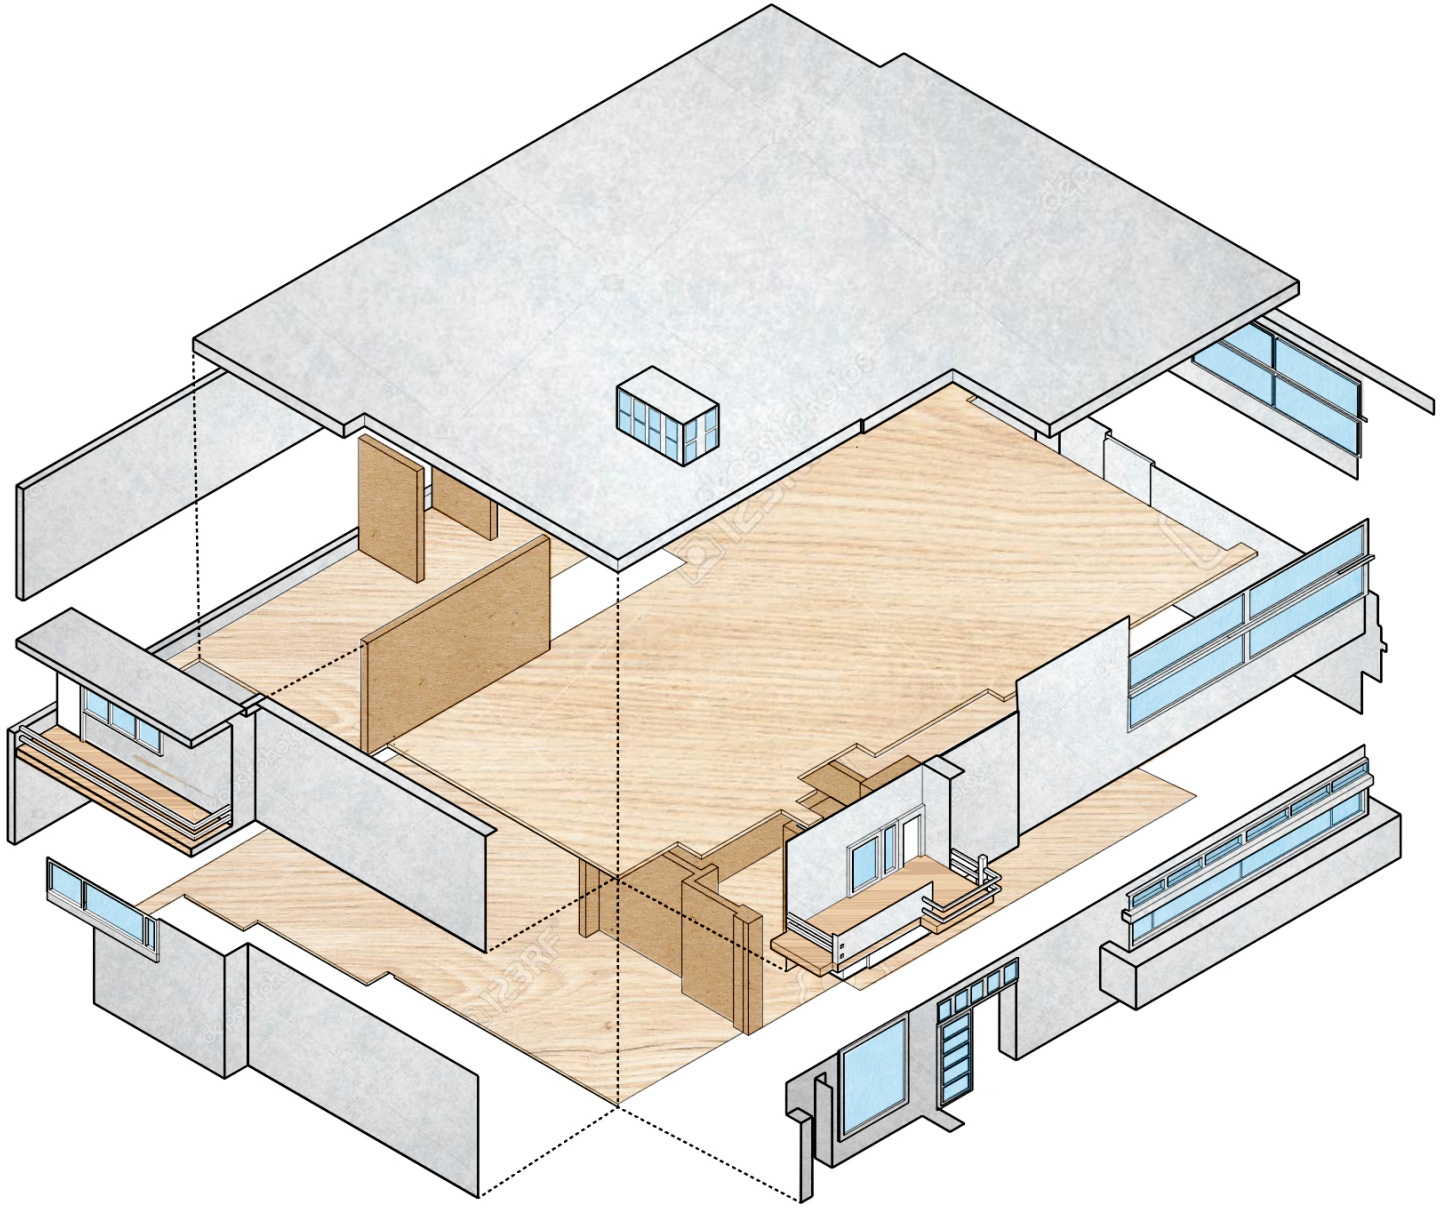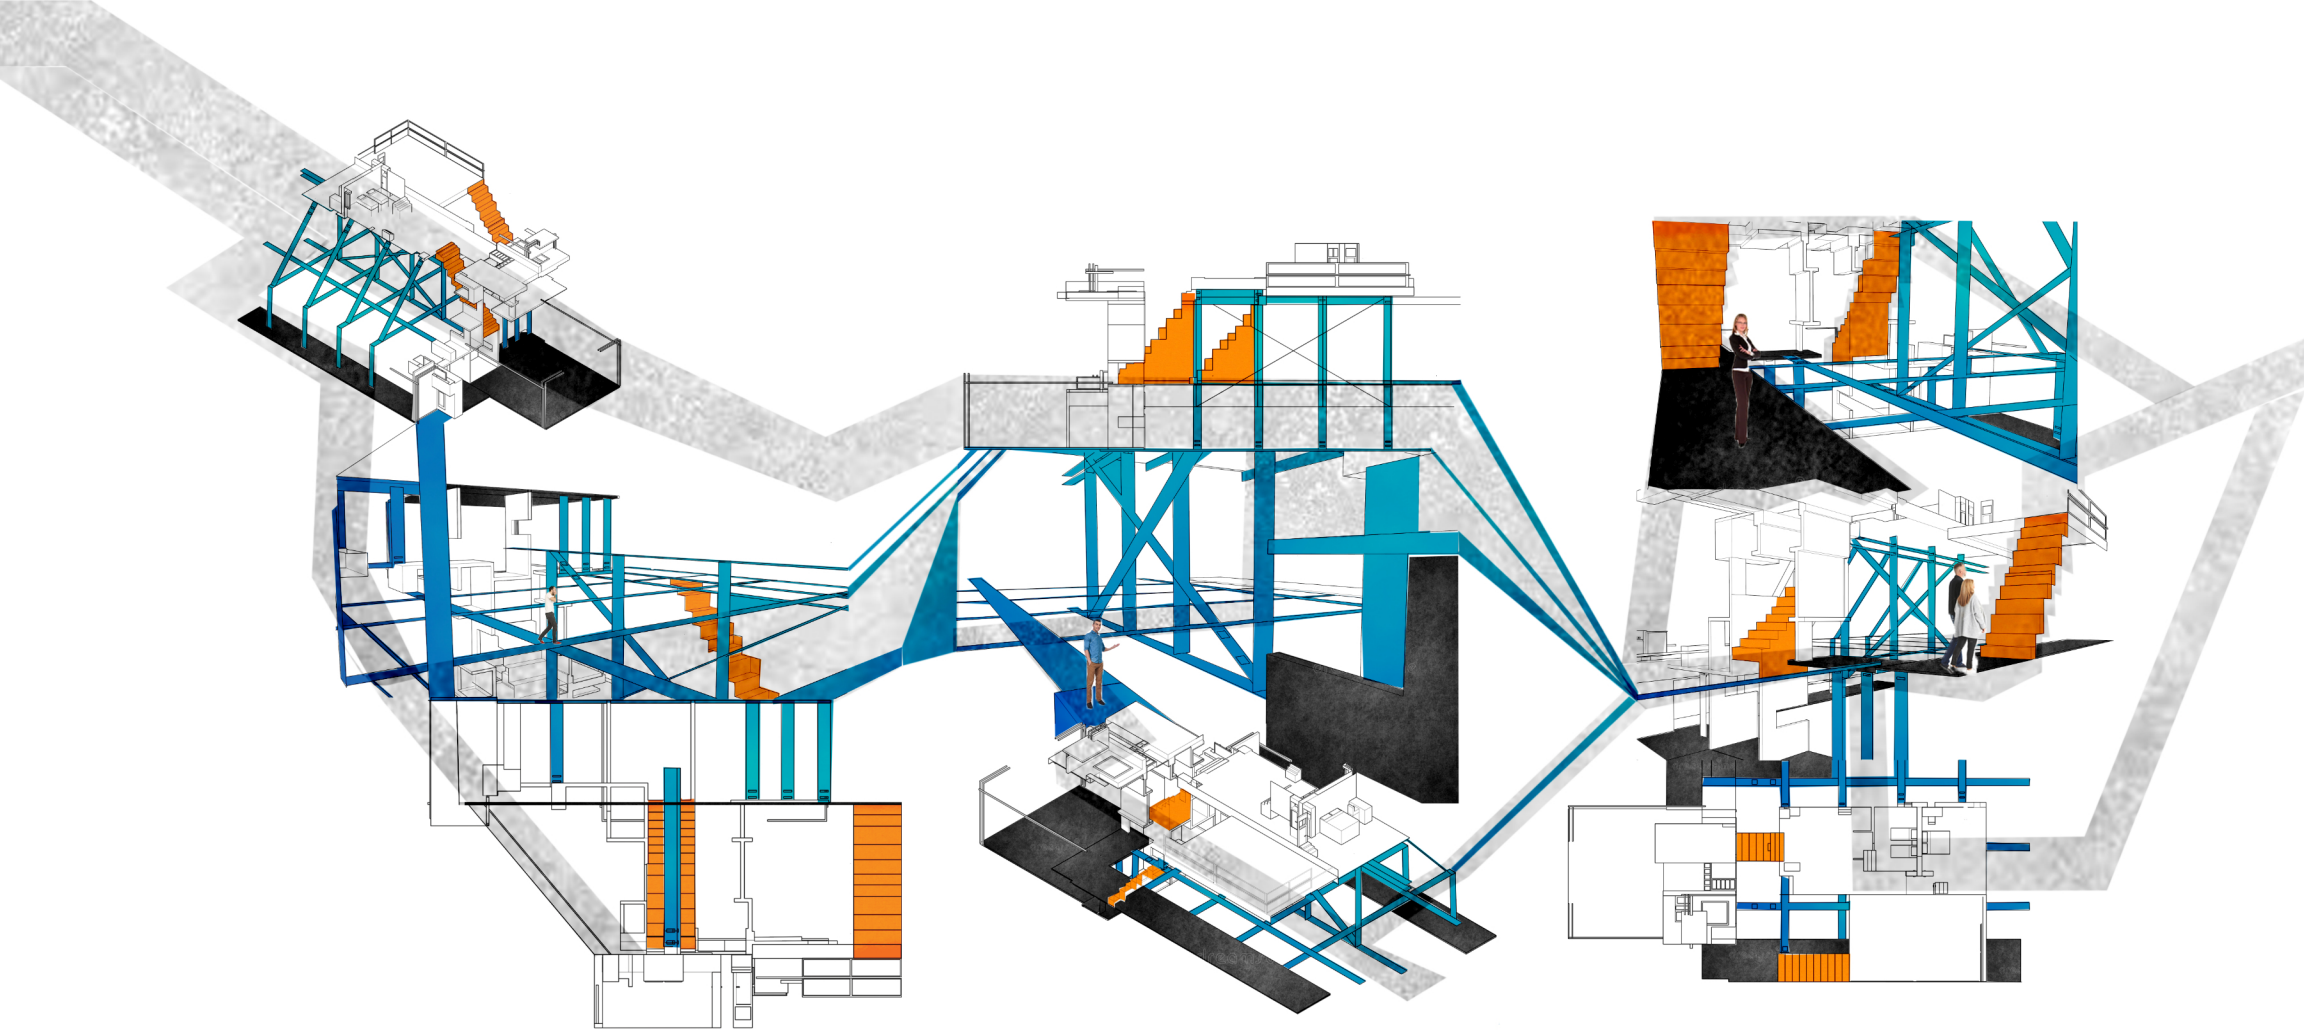
TO SURROUND